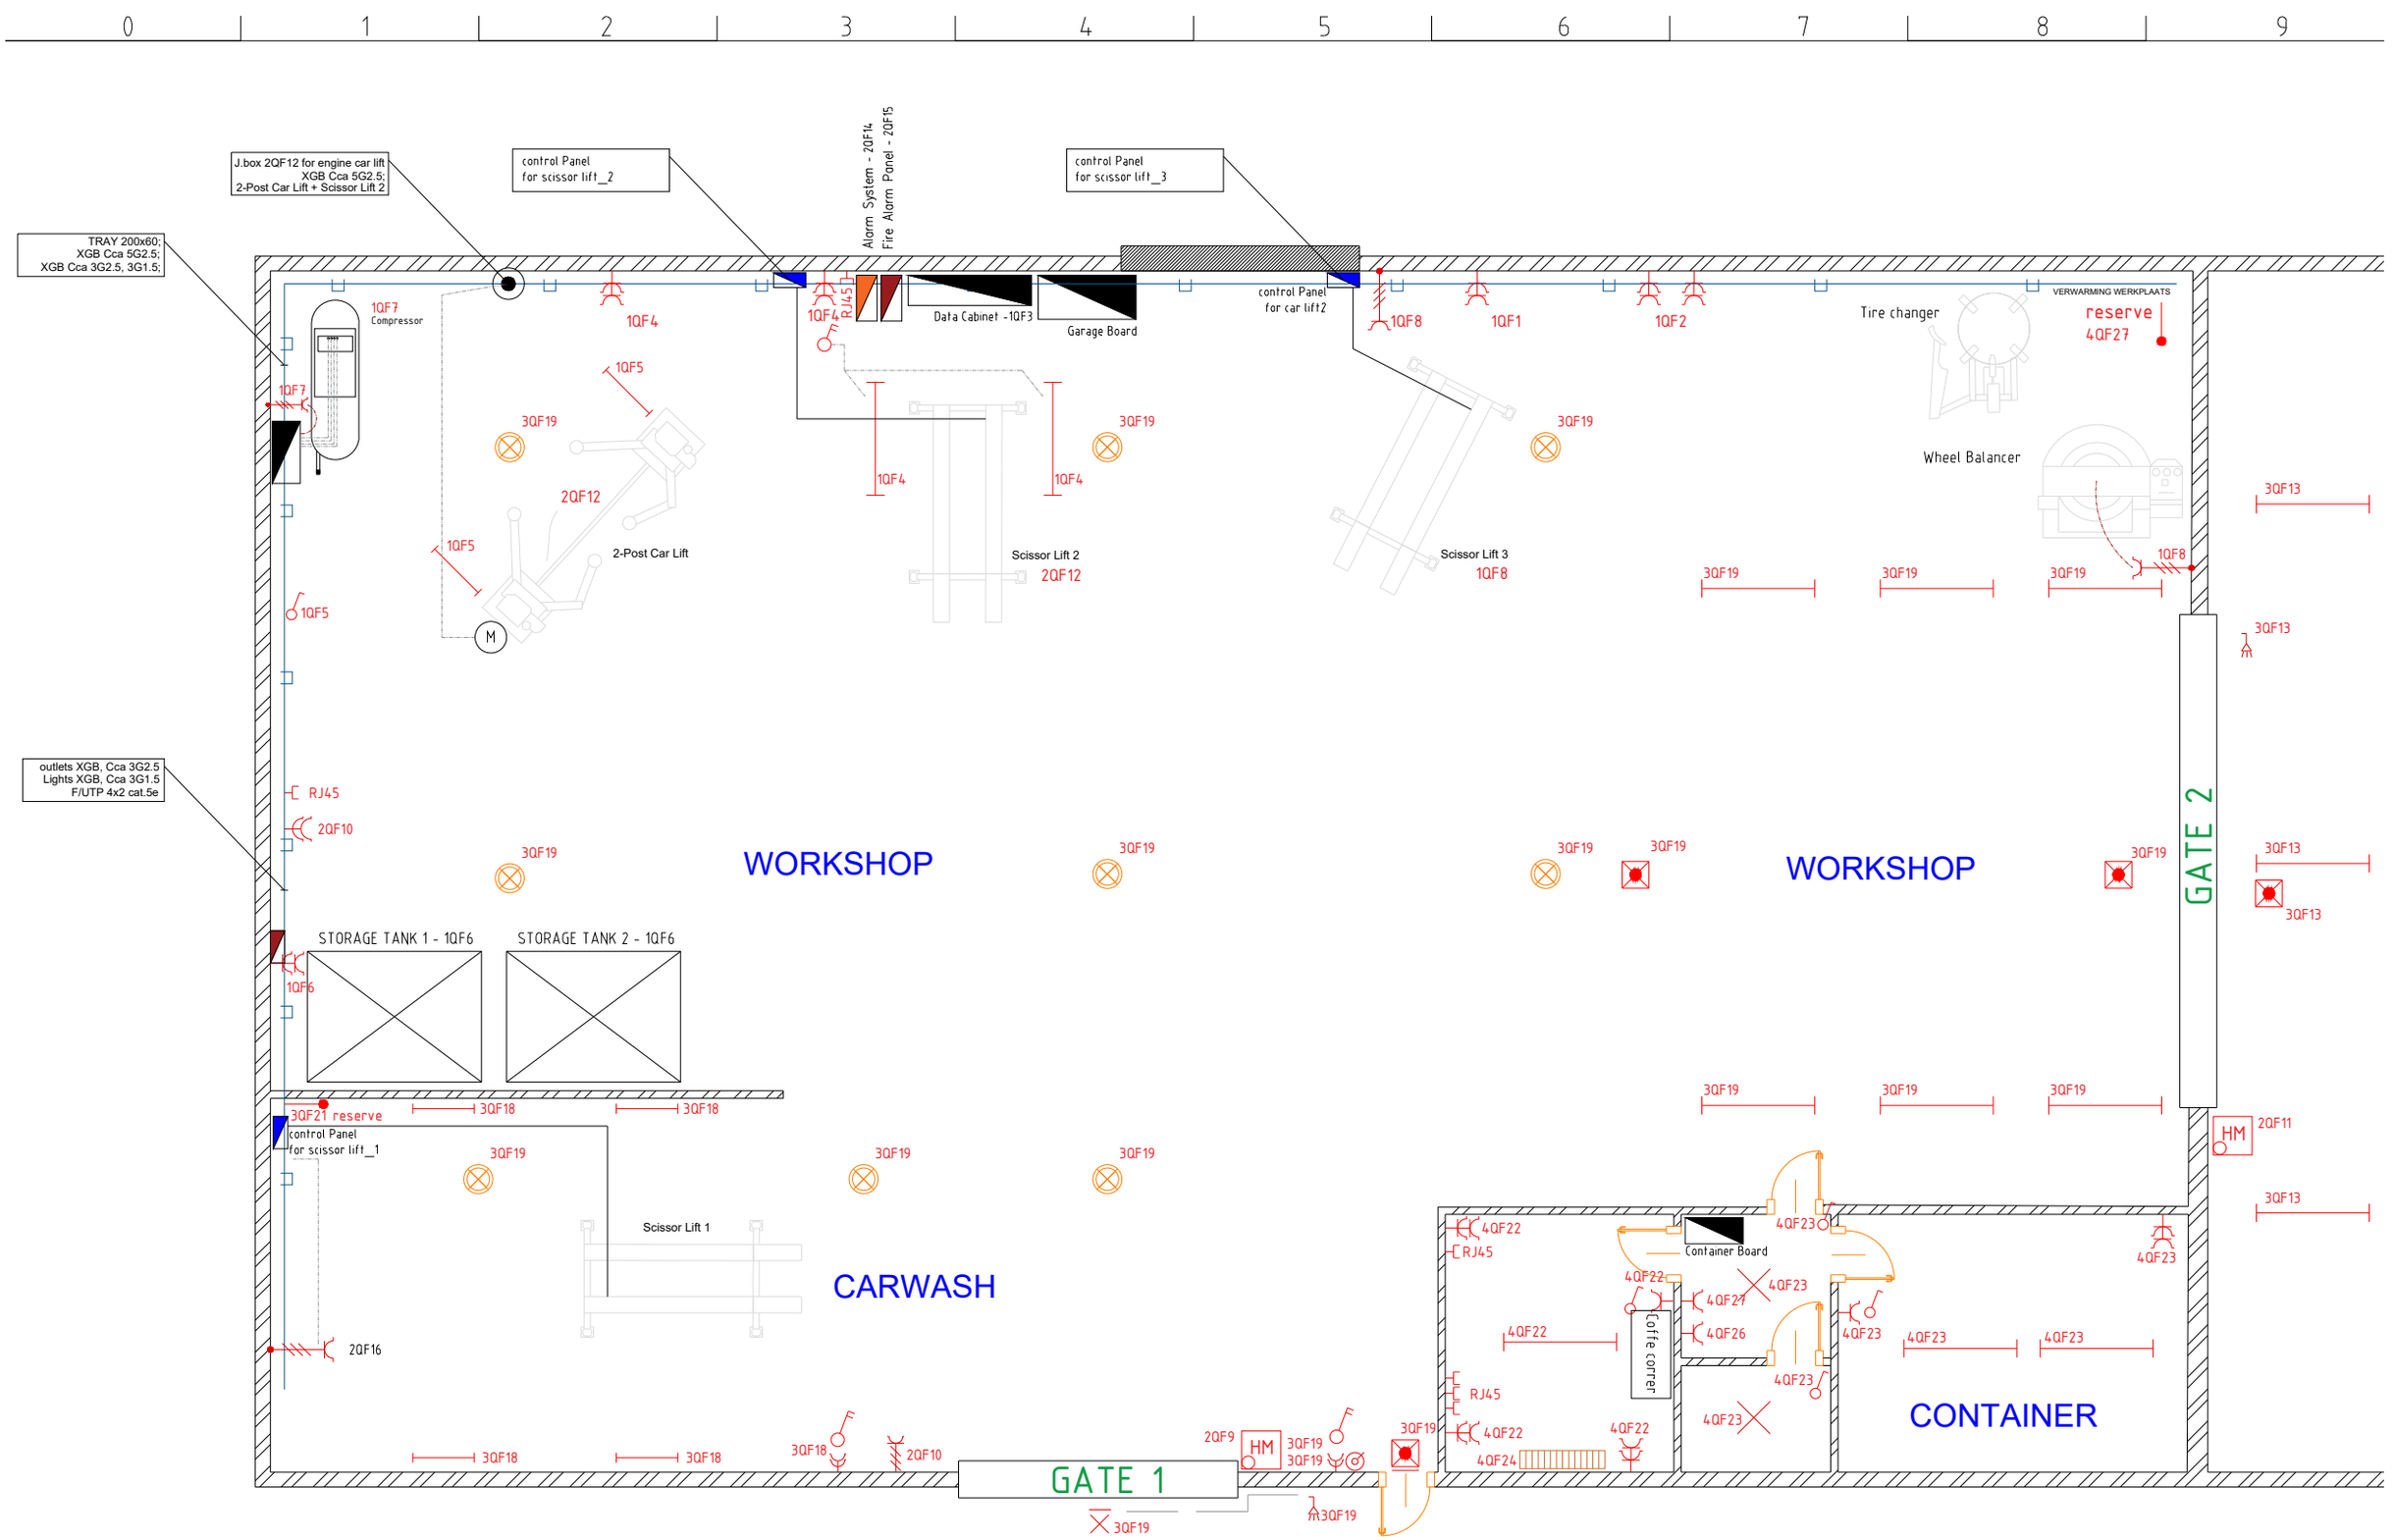
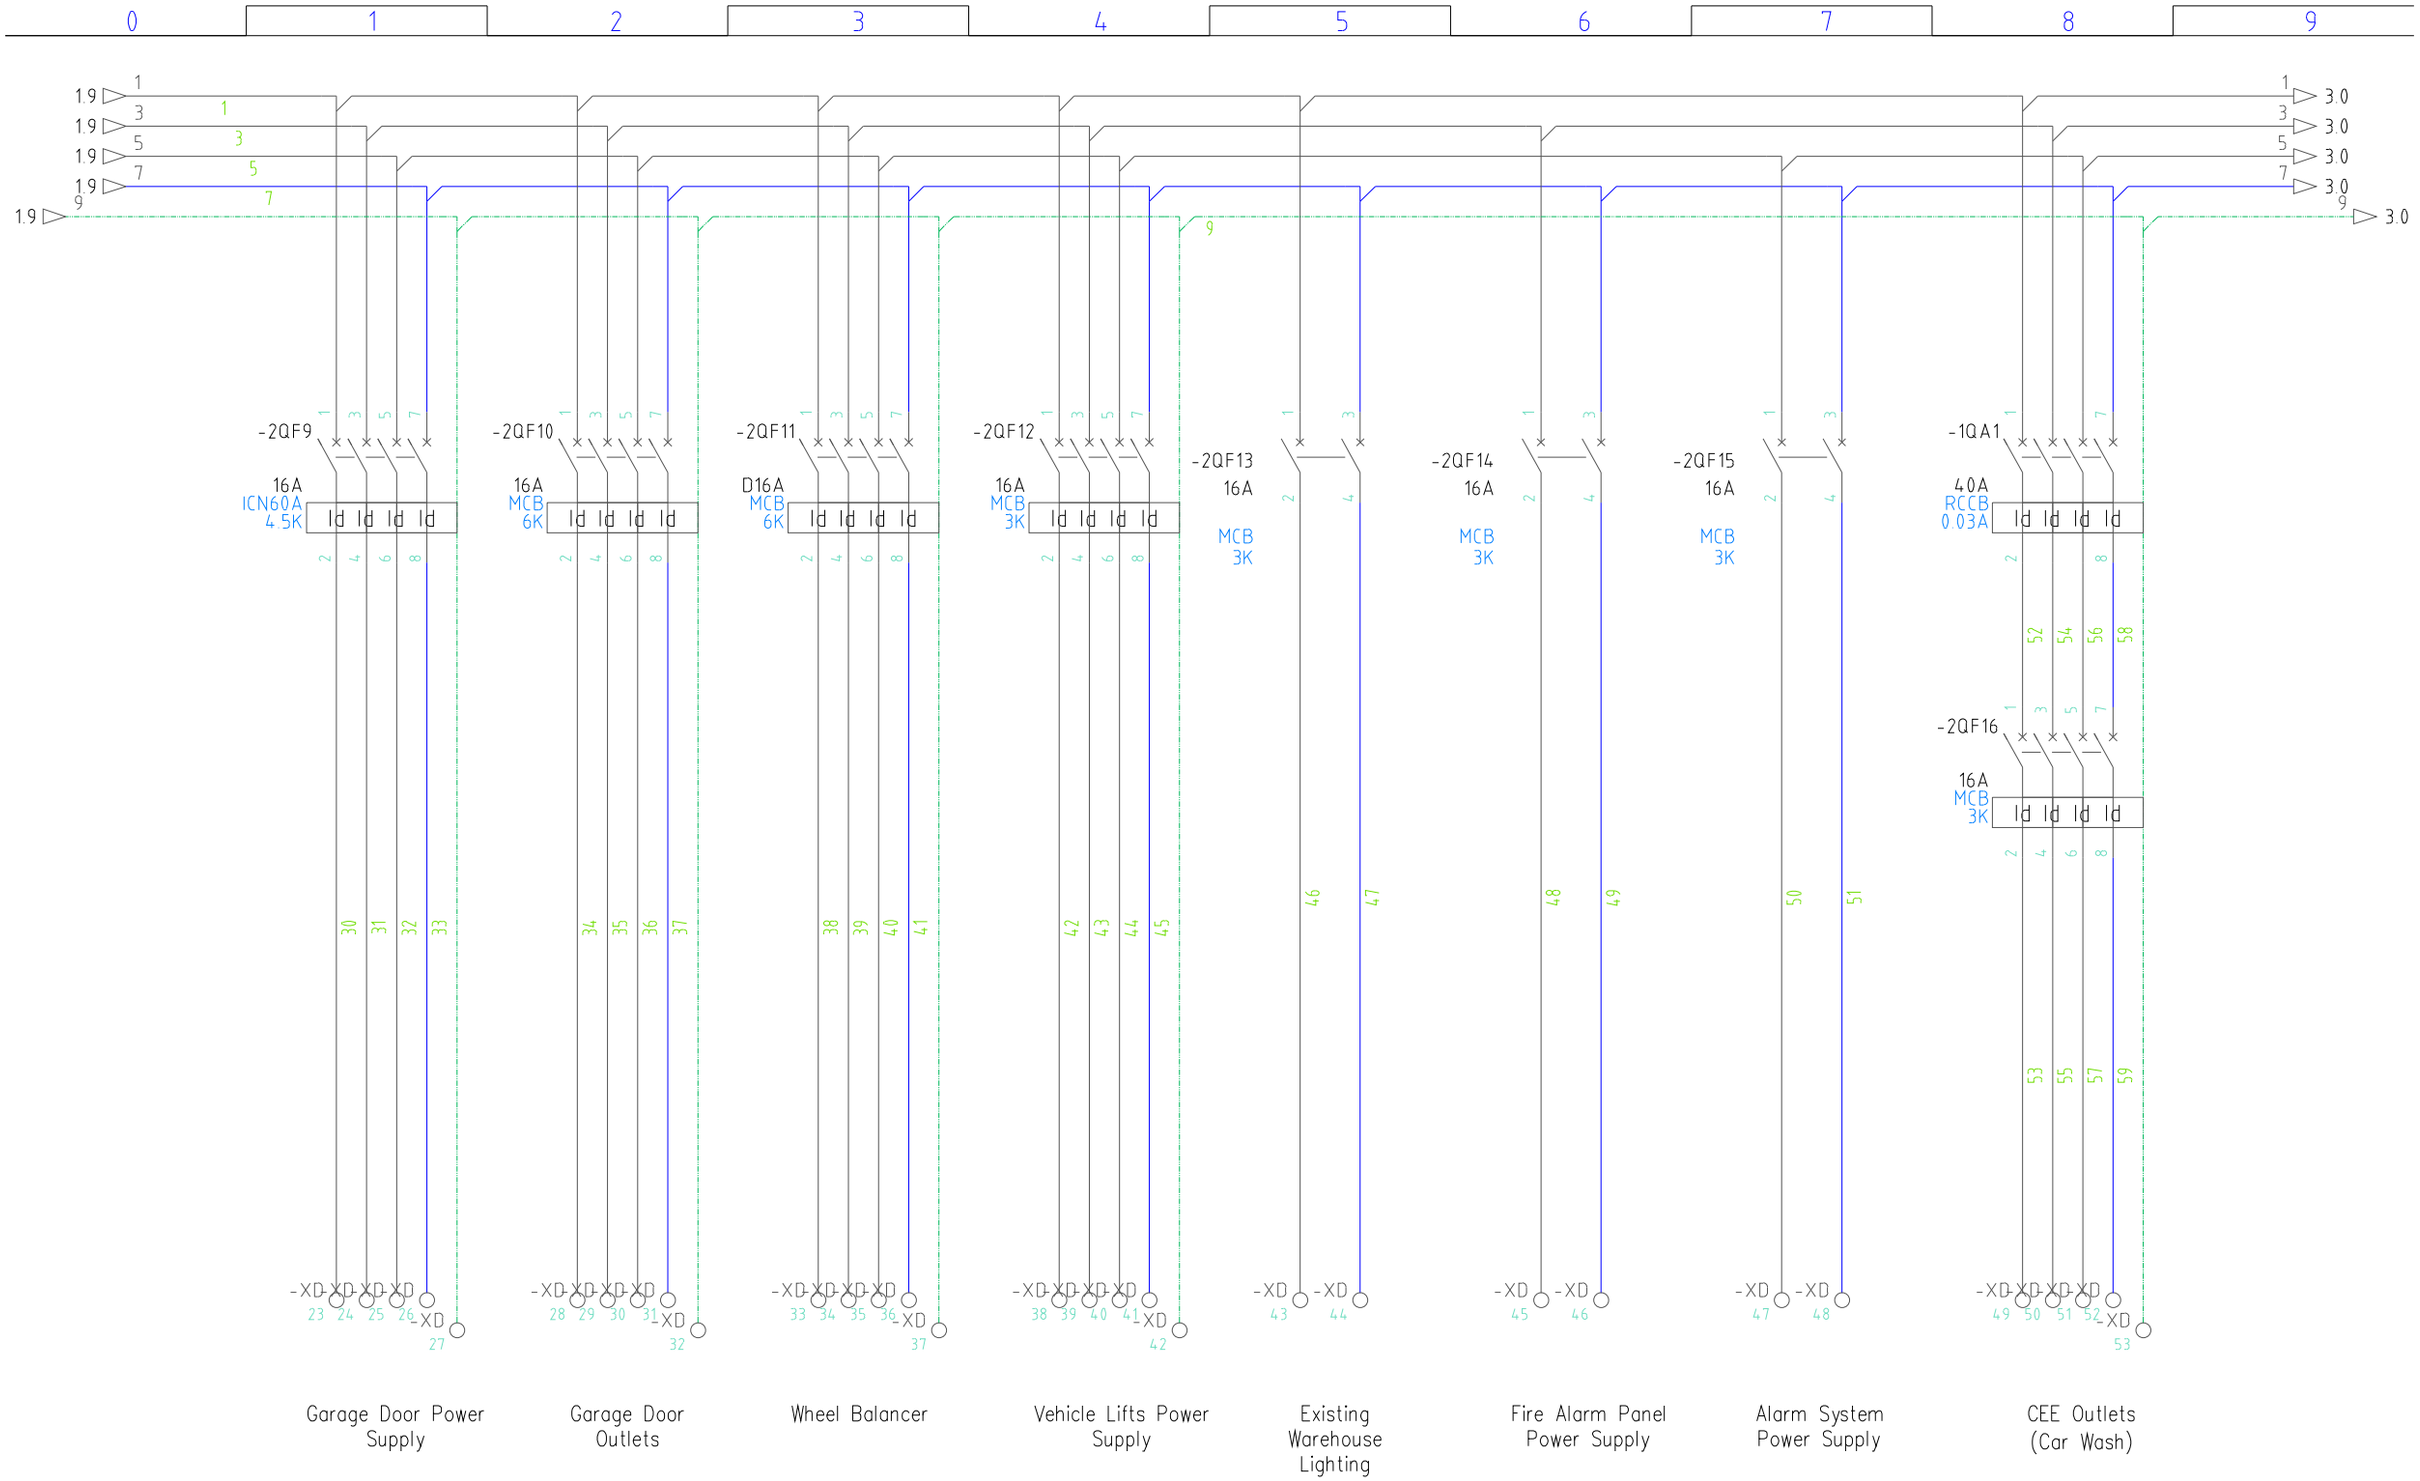


ARCADIAN | Electrical engineering

Workshop power and cable routes | Portfolio excerpt


0
1
2
3
4
5
6
7
8
9
-1QF1
20A
MCB
3K
-1QF2
20A
MCB
3K
-1QF3
16A
MCB
3K
-1QF4
16A
MCB
6K
-1QF5
16A
MCB
6K
-1QF6
20A
MCB
6K
-1QF7
16A
ICN60A
4.5K
-1QF8
16A
ICN60A
4.5K
2.0
2.0
2.0
2.0
2
Local Energy
Meter kWh
-1QA0
40A
RCCB
0.3A
-XD
Workshop outlets
Workshop outlets
Data Cabinet outlets
Workshop outlets + Lighting (Scissor Lift)
Stopcontacten werkplaats + verlichting scissor Lift
Oil Storage tank 1,2
Compressor
Scissor Lift 3
kWh
-PE
Location: CTD BVBA
Meter and earthing located elsewhere in the building


0
1
2
3
4
5
6
7
8
9
1.9
3.0
-2QF9
16A
ICN60A
4.5K
-2QF10
16A
MCB
6K
-2QF11
D16A
MCB
6K
-2QF12
16A
MCB
3K
-2QF13
16A
MCB
3K
-2QF14
16A
MCB
3K
-2QF15
16A
MCB
3K
-1QA1
40A
RCCB
0.03A
-2QF16
16A
MCB
3K
-XD
Garage Door Power Supply
Garage Door Outlets
Wheel Balancer
Vehicle Lifts Power Supply
Existing Warehouse Lighting
Fire Alarm Panel Power Supply
Alarm System Power Supply
CEE Outlets (Car Wash)