
Number	Name
+0.0	Garage
+0.1	Inkomhal
+0.2	Bureau
+0.3	Vestiaire
+0.4	WC
+0.5	Office
+0.6	Leefruimte
+0.7	Eetkamer
+0.8	Terras
+0.9	Zwembad (Sauna)
+0.10	Leefruimte
+0.11	Keuken
+0.12	Bijkeuken
+0.13	Traphal kelder

DL1	G01	2	+0,5
	G02	2	+0,6
	G03	3	+0,7
	G04	2	+0,7
	G05	2	+0,7
	G06	2	+0,7
	G07	2	+0,7
	G08	2	+0,7
	G09	3	+0,7
	G10	2	+0,7
	G11	3	+0,12
	G12	2	+0,12
	G13	2	+0,12
	G14	2	+0,13
	G15	3	+0,1
	G16	2	+0,1
	G17	2	+0,2
	G18	2	+0,2
	G19	3	+0,3
	G20	1	+0,3
	G20.1	1	+0,4

Line	Group	PCS	Room	Description
DMM1	G-01	1	+0,7	PENDEL Eetkamer +00
	G-02	2	+0,1	WL Inkomhal, Traphal +00
DMM2	G-01	4	+0,4	WL (WC, Vestiaire) +00
	G-02	2	+1,4	Master suit PENDEL +01
DMM3	G-01	1	+1,3	Office +00
	G-02	2	+1,3	Master suit(pendel) +01
DMM4	G-01	2	+1,2	Master Badkamer +01
	G-02		+1,5	Nachthal +01
DMM5	G-01	2	+1,2	Master suit +01
	G-02	3	+1,8	Slaapkamer 4 +01
SW1	G-01	2	+0,0	Garage
	G-02	3		Outside
	G-03			
	G-04			
	G-05			
	G-06			
LED	4QF3			

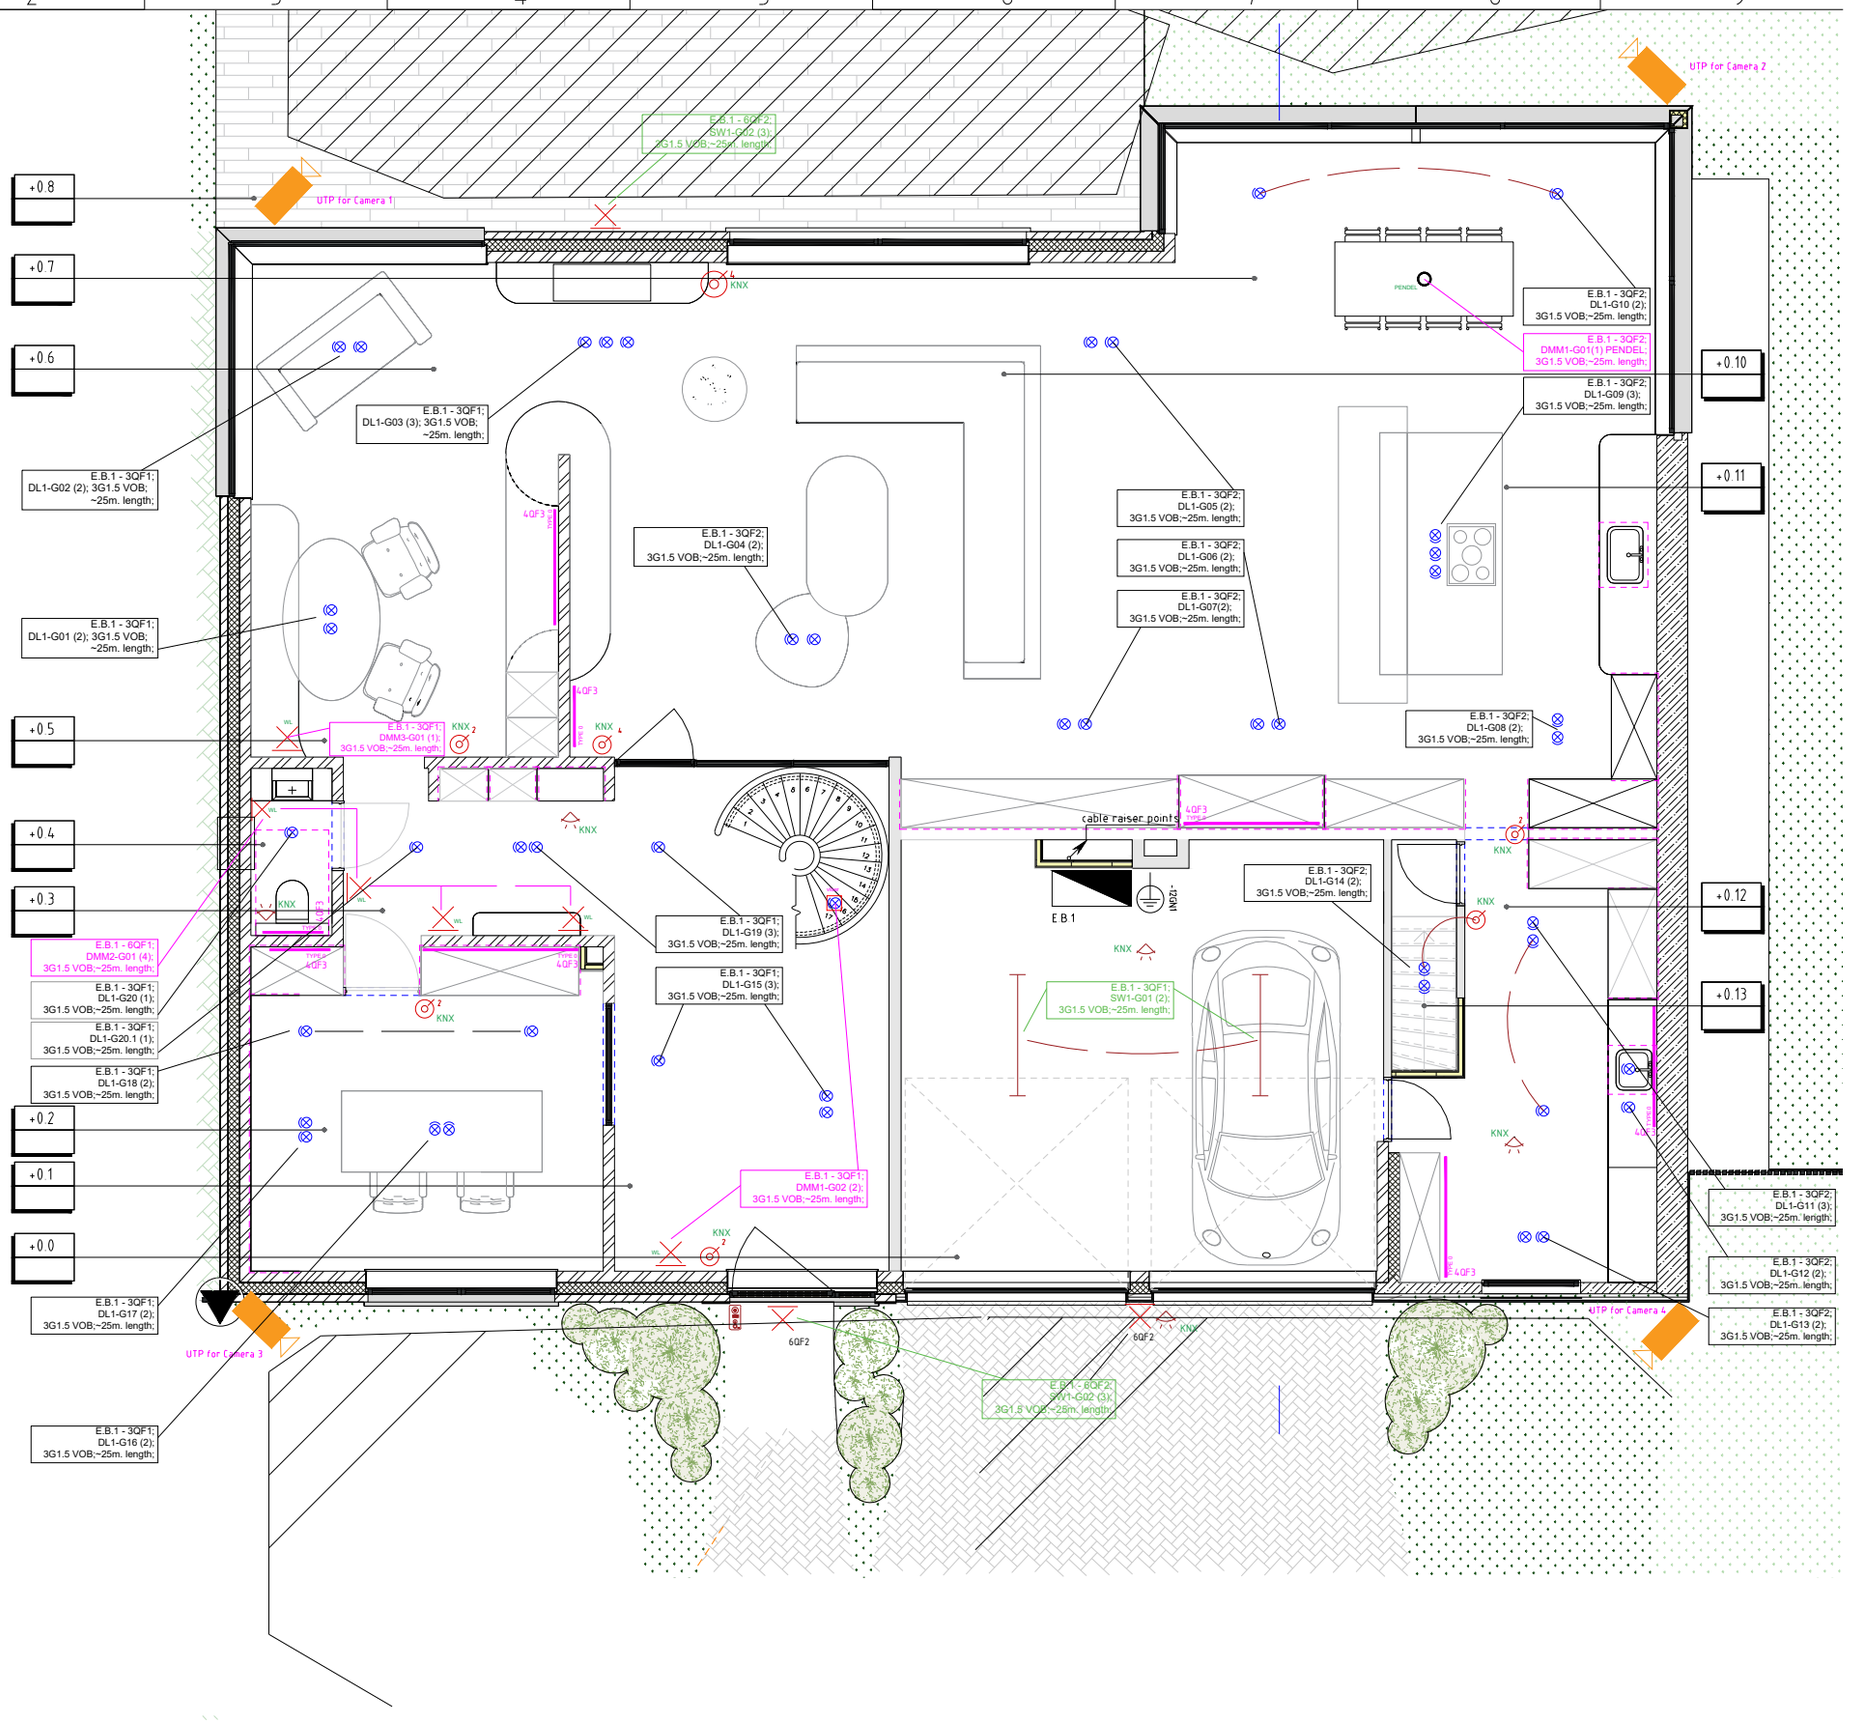

ARCADIAN | Electrical engineering


DALI lighting layout and control groups | Portfolio excerpt


Number	Name
+0.0	Garage
+0.1	Inkomhal
+0.2	Bureau
+0.3	Vestiaire
+0.4	WC
+0.5	Office
+0.6	Leefruimte
+0.7	Eetkamer
+0.8	Terras
+0.9	Zwembad (Sauna)
+0.10	Leefruimte
+0.11	Keuken
+0.12	Bijkeuken
+0.13	Traphal kelder

×floor level +5cm compared to existing (new floor plate) - see floor plan for specificationns of the transition floor finish (under sliding door)

RCCB 300mA
1QA1
- RCCB 1QA4, 1QA7
- RCCB 1QA8
  - 3QF1 - 3QF8
- RCCB 1QA10
  - 6QF1 - 6QF4

×level and type of ceilings and plaster walls are not determined!!!

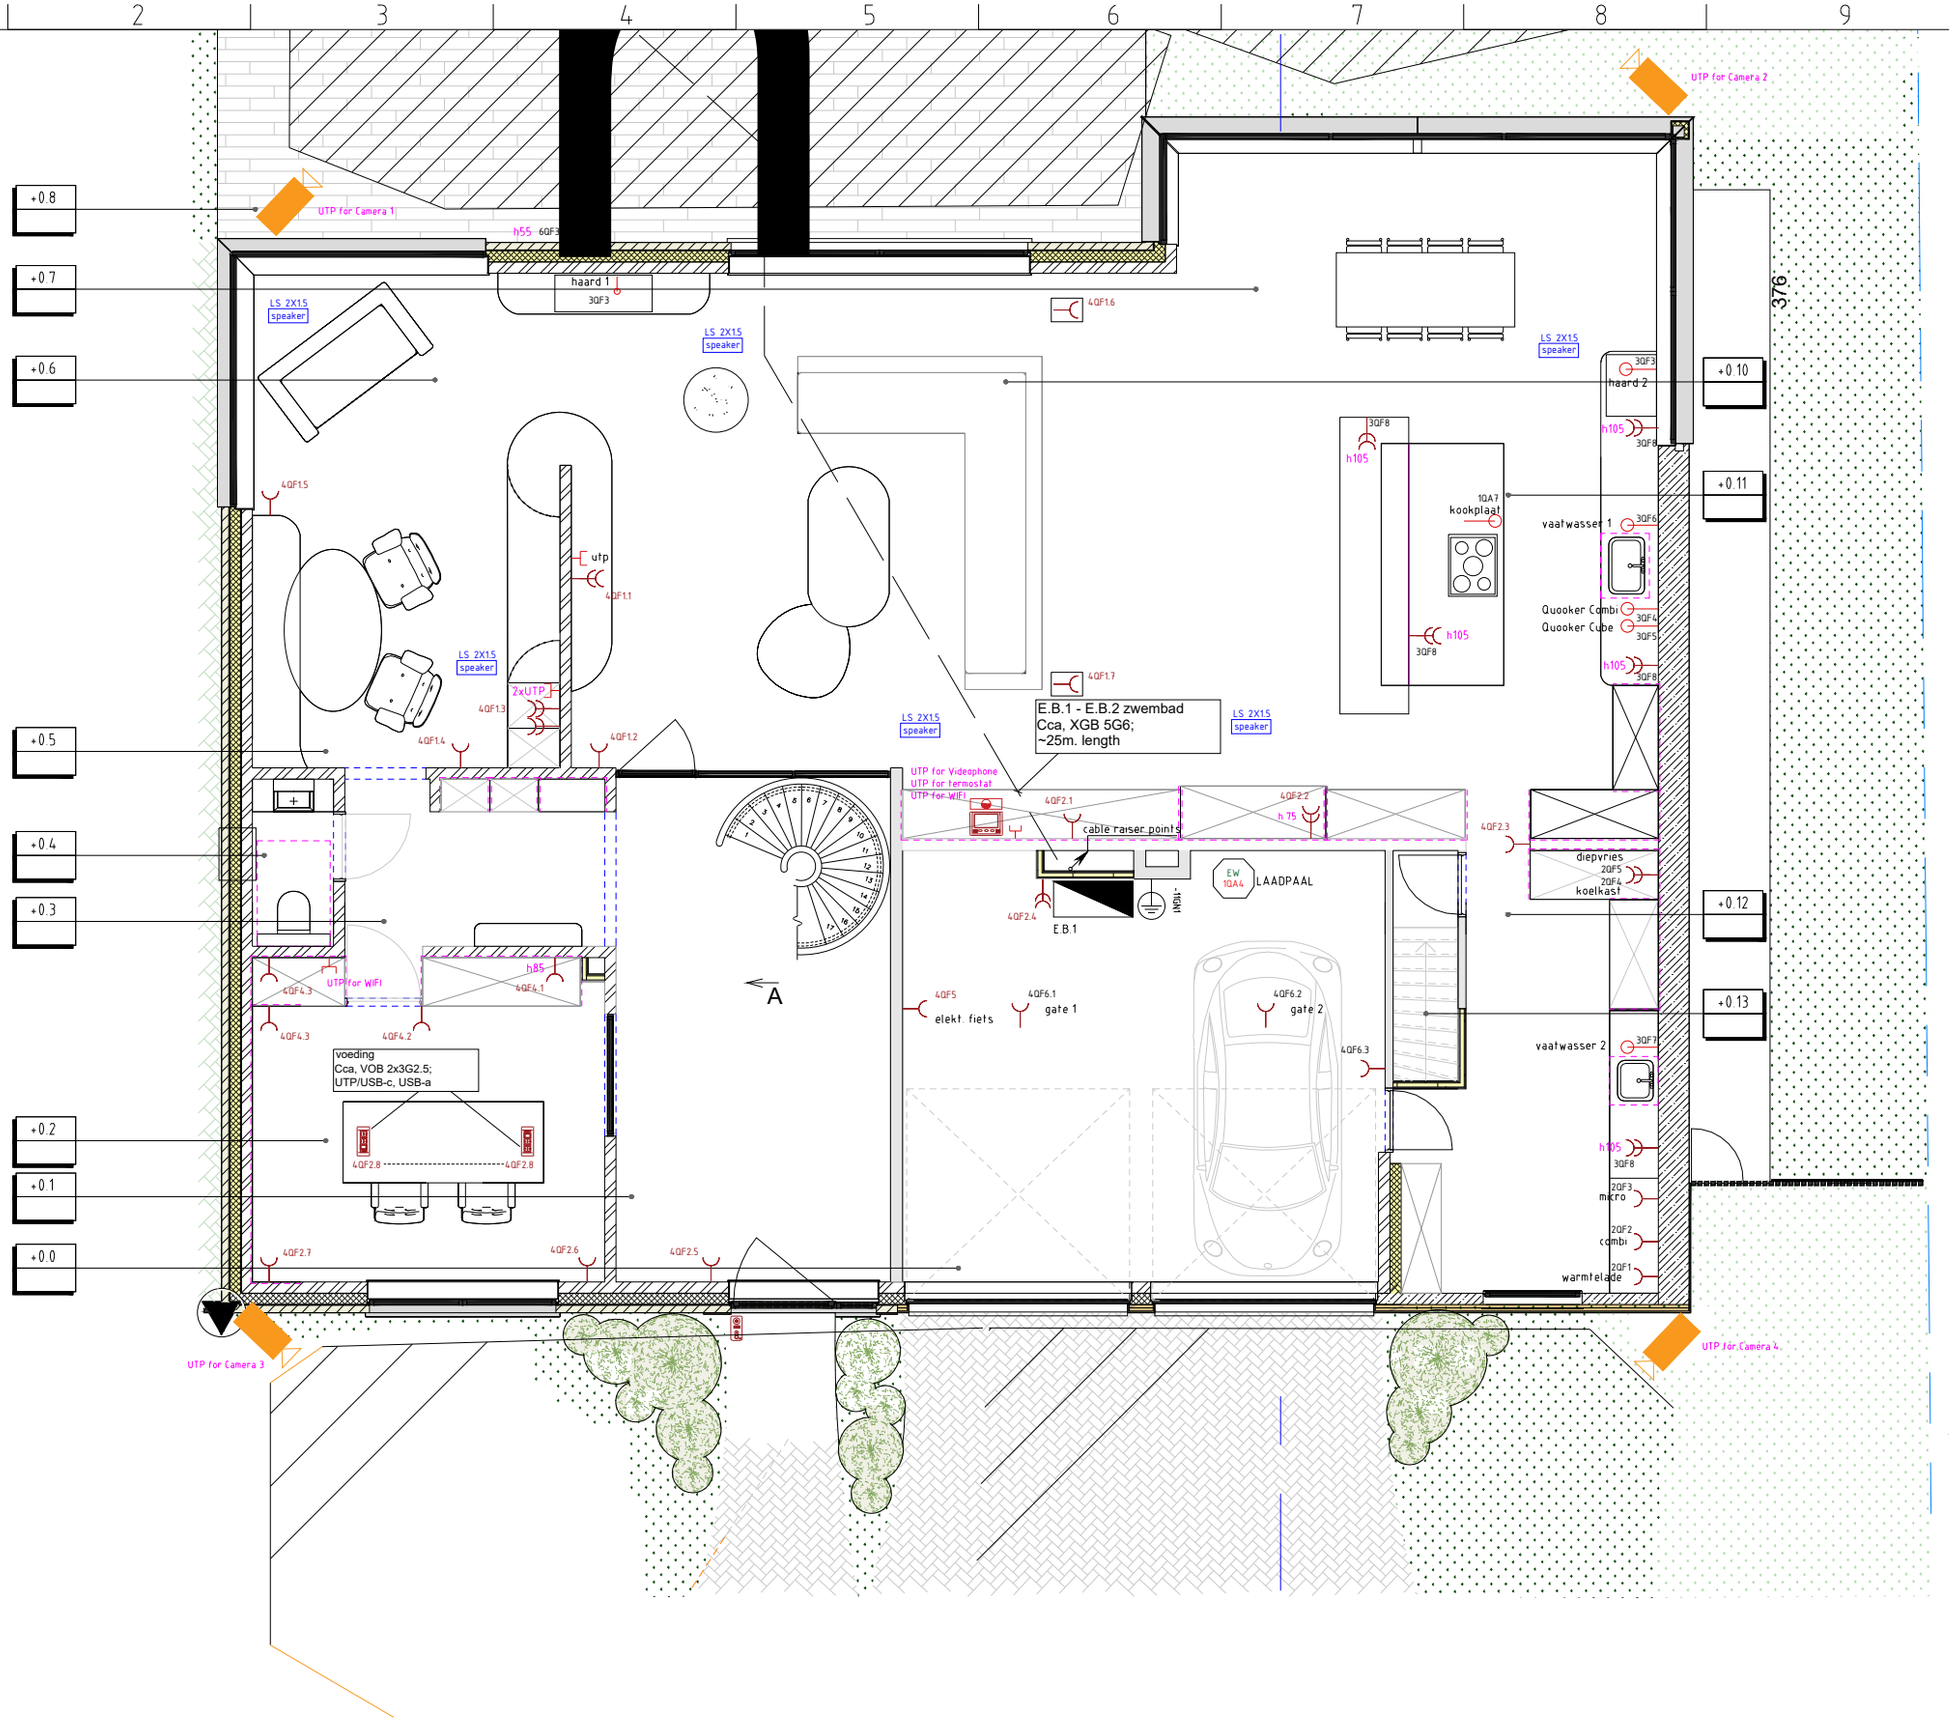

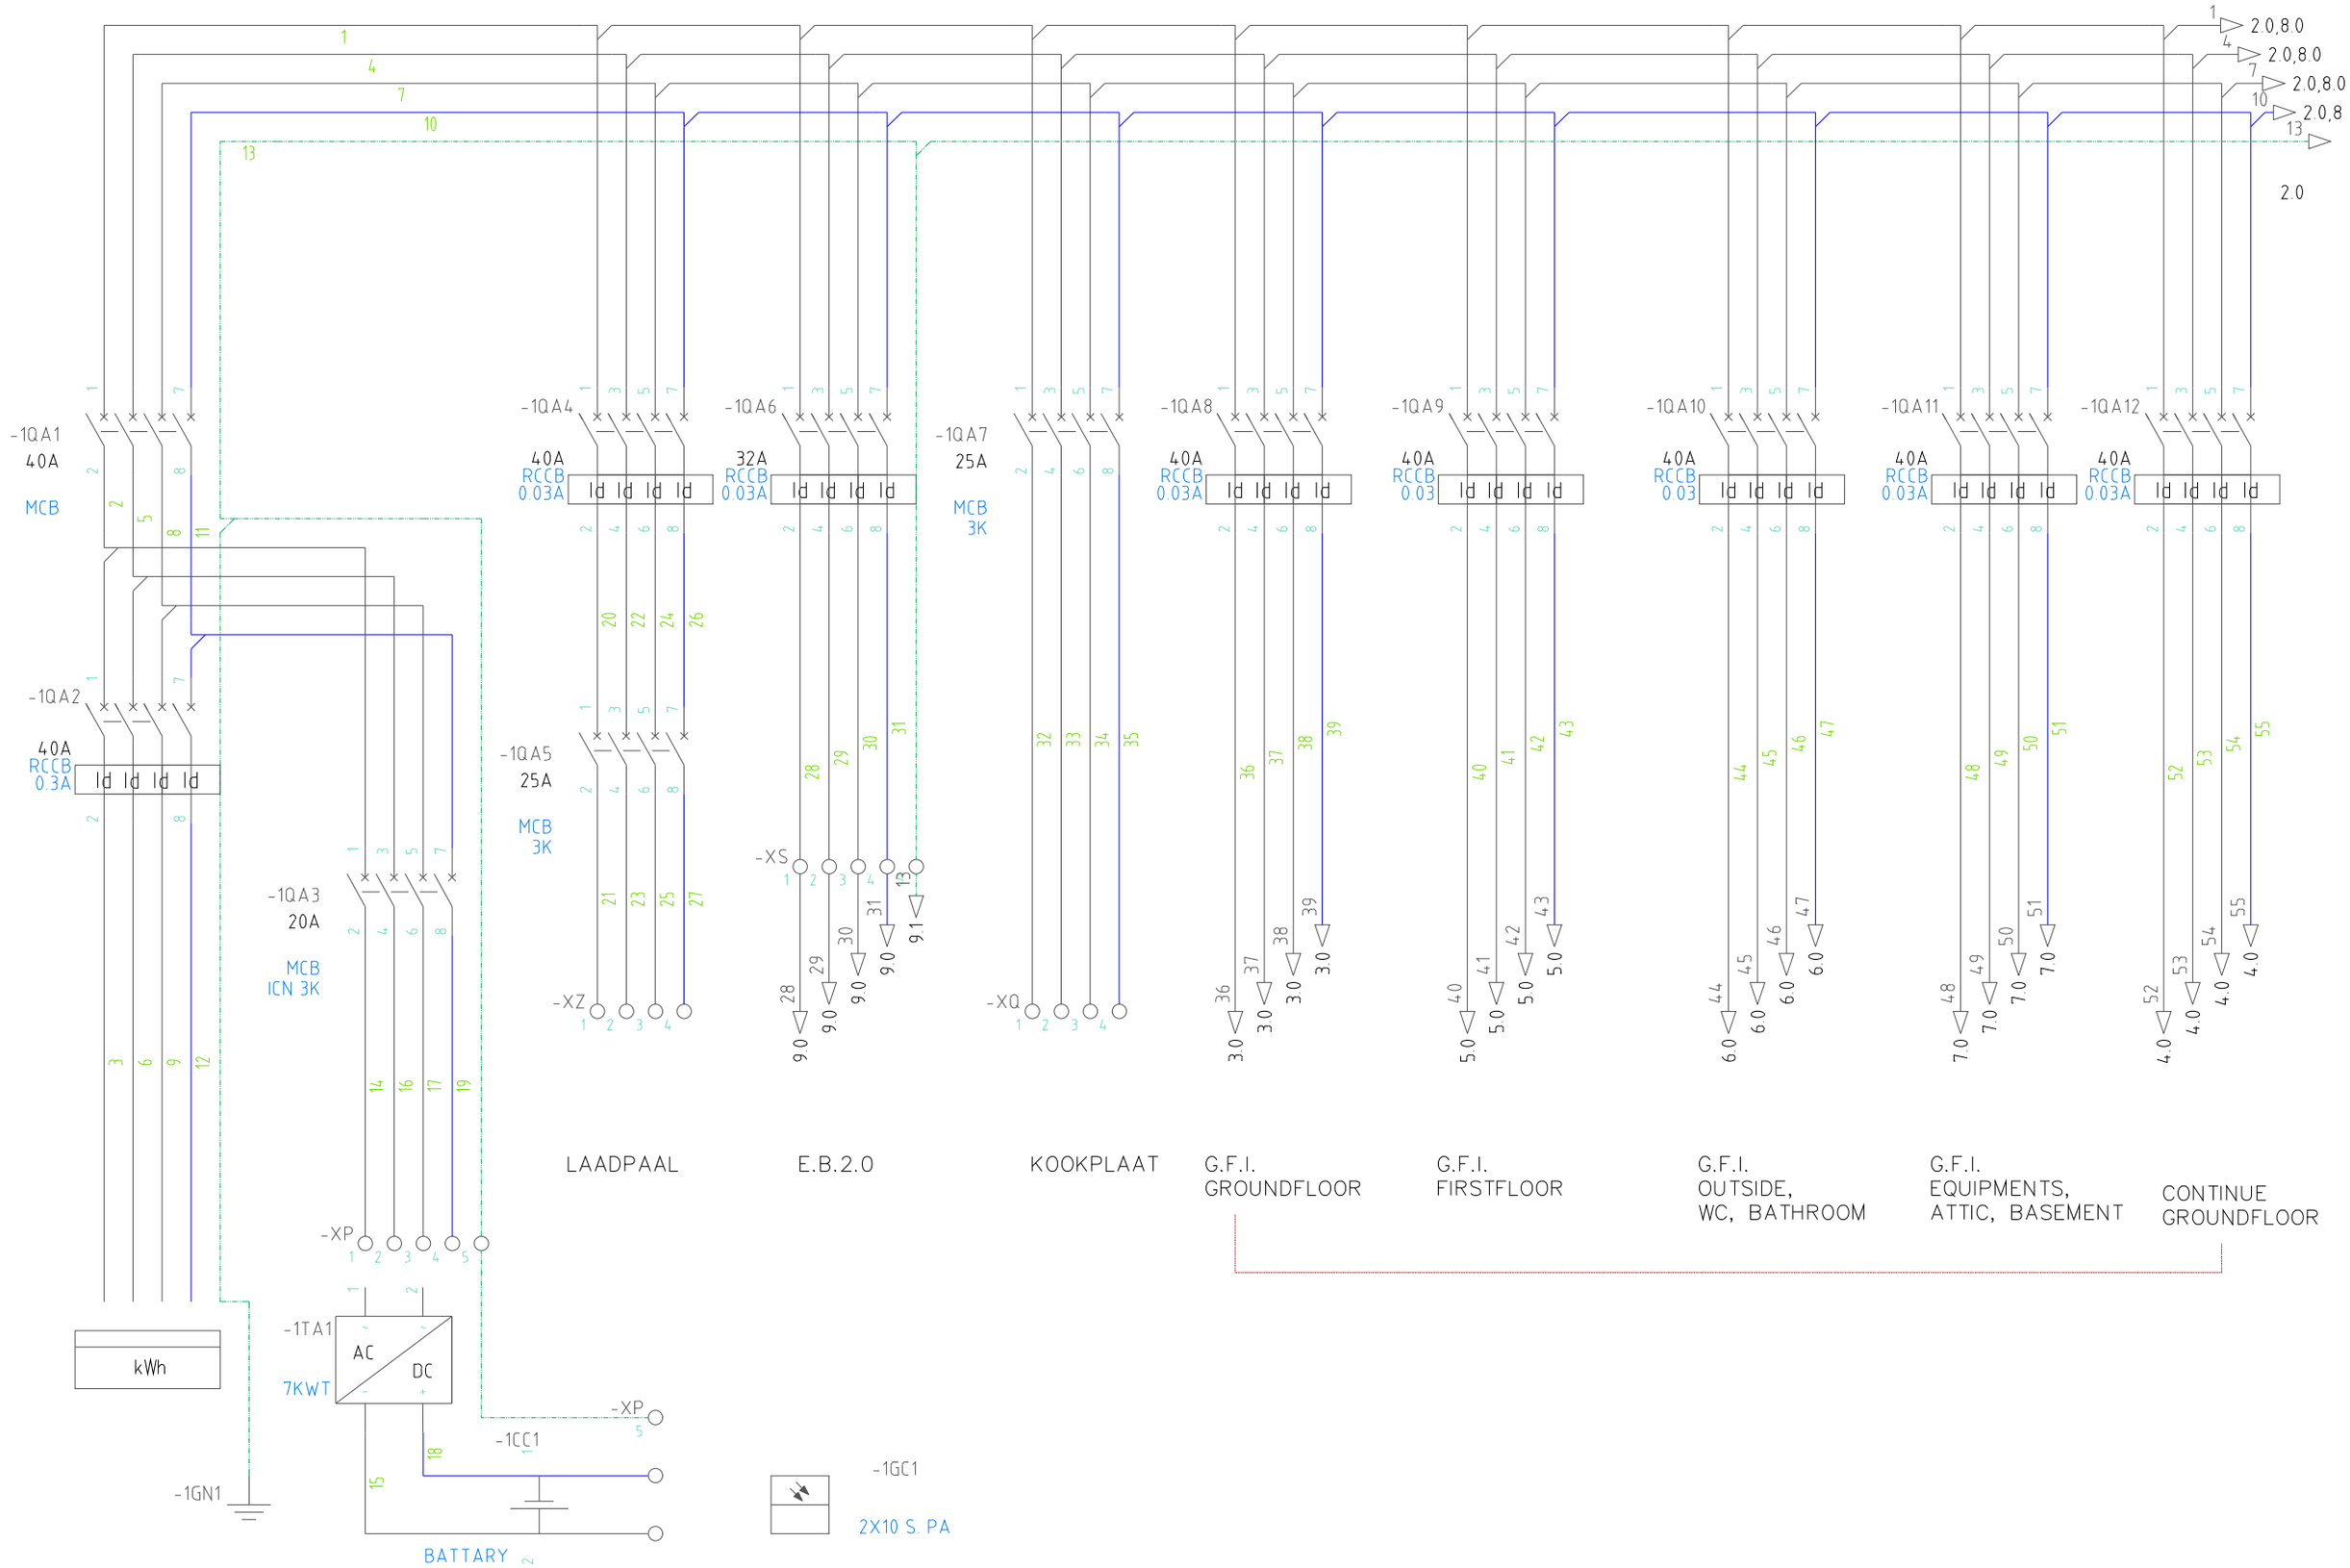

ARCADIAN | Electrical engineering

Single-line diagram: distribution and protection | Portfolio excerpt