Woning B
Gelijkvloers

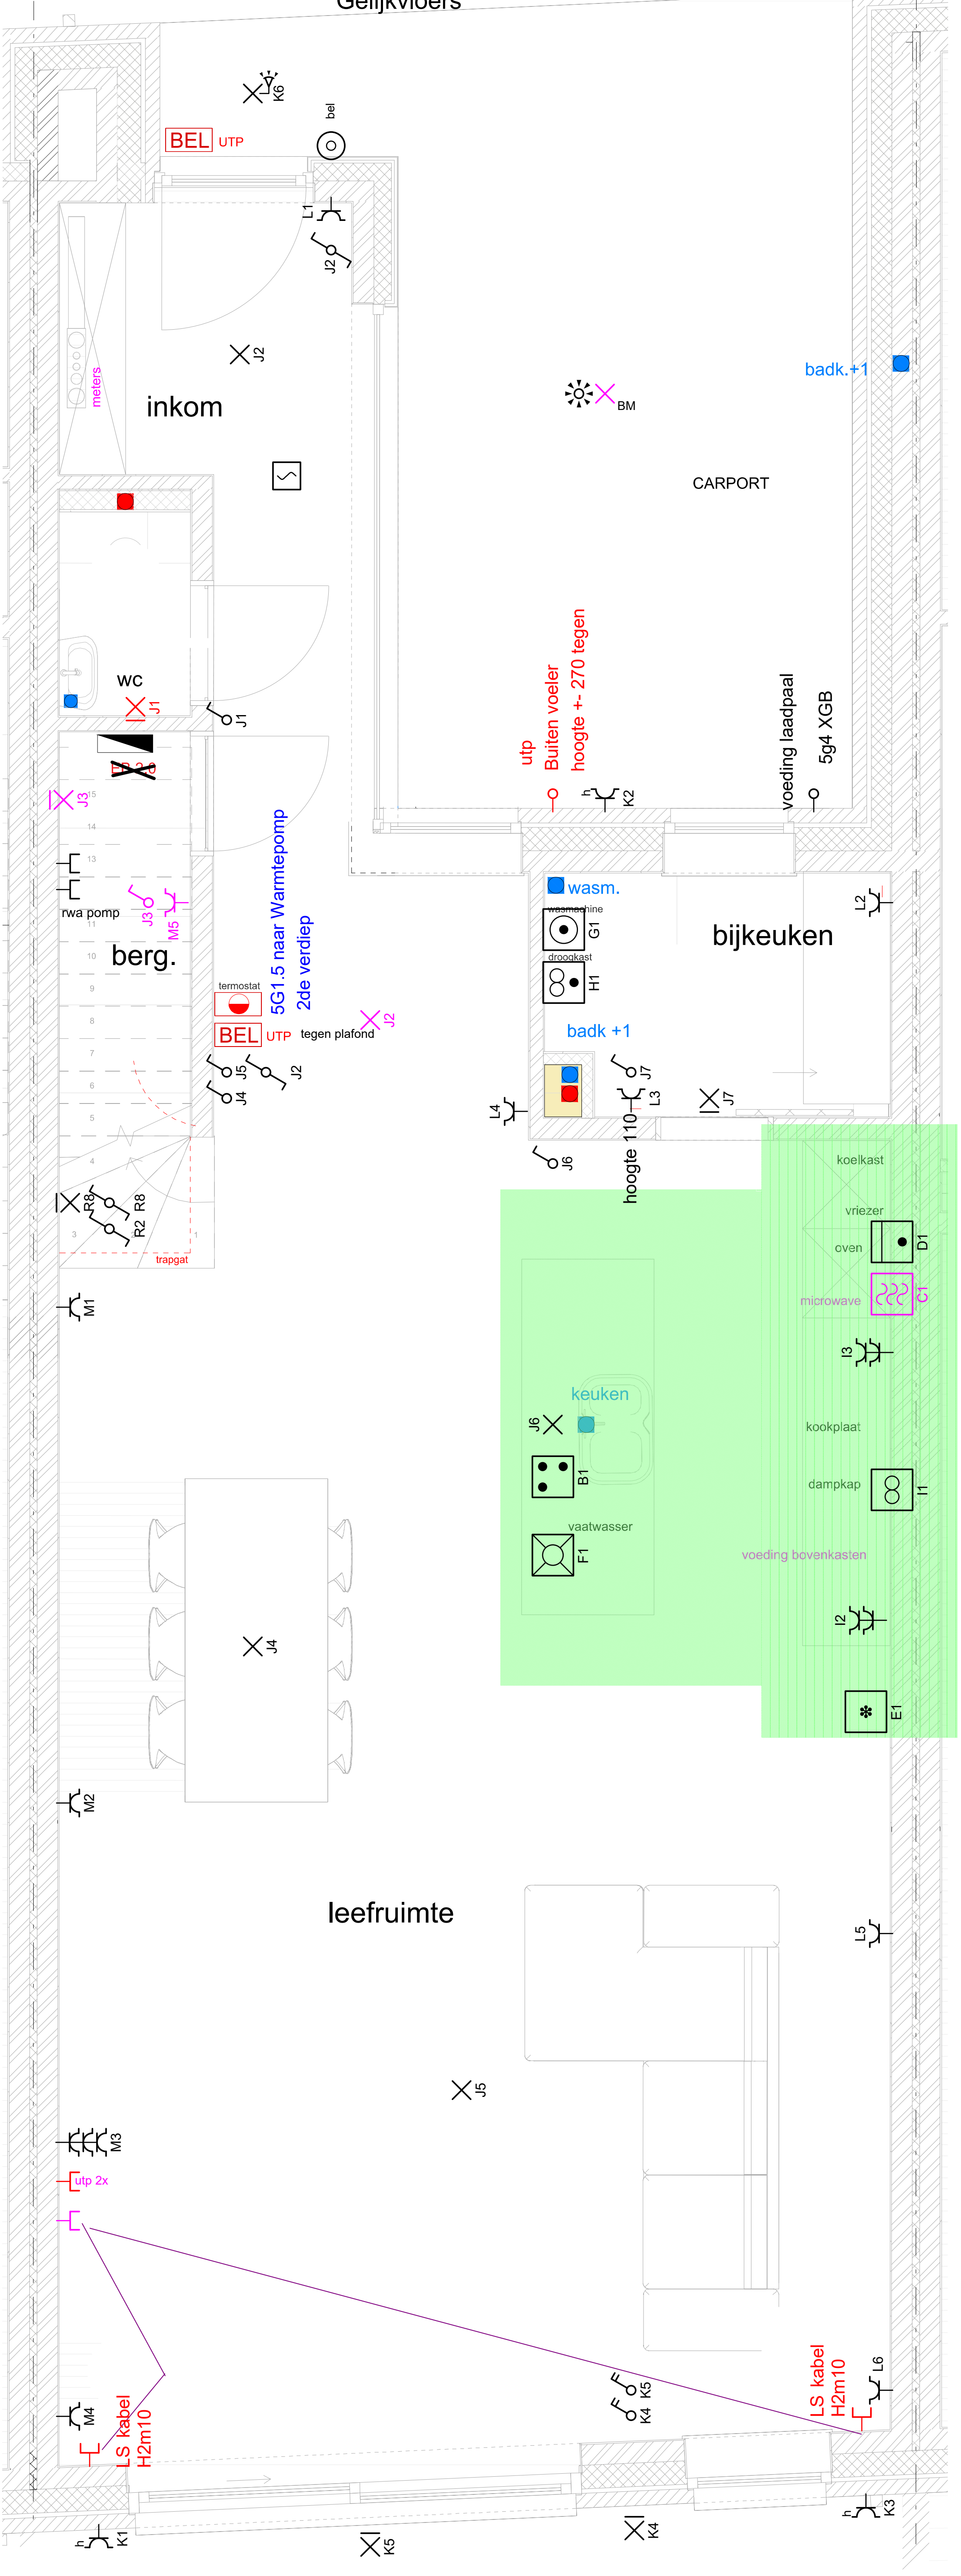
K6
BEL
UTP
bel
L1
J2
J2
meters
inkom
BM
badk.+1
CARPORT
wc
J1
J1
J3
rwa pomp
J3
M5
berg.
5G1.5 naar Warmtepomp
2de verdiep
termostat
BEL
UTP
tegen plafond
J2
J5
J2
J4
R8
R2
trapgat
utp
Buiten voeler
hoogte +- 270 tegen
K2
voeding laadpaal
5g4 XGB
wasm.
wasmachine
G1
droogkast
H1
bijkeuken
L2
badk +1
J7
L3
J7
L4
J6
hoogte 110
koelkast
vriezer
oven
D1
microwave
C1
I3
keuken
J6
B1
vaatwasser
F1
kookplaat
dampkap
I1
voeding bovenkasten
I2
E1
Volgens keuken plan
M1
J4
M2
leefruimte
L5
J5
M3
utp 2x
K5
K4
L6
LS kabel
H2m10
M4
LS kabel
H2m10
K1
K5
K4
K3

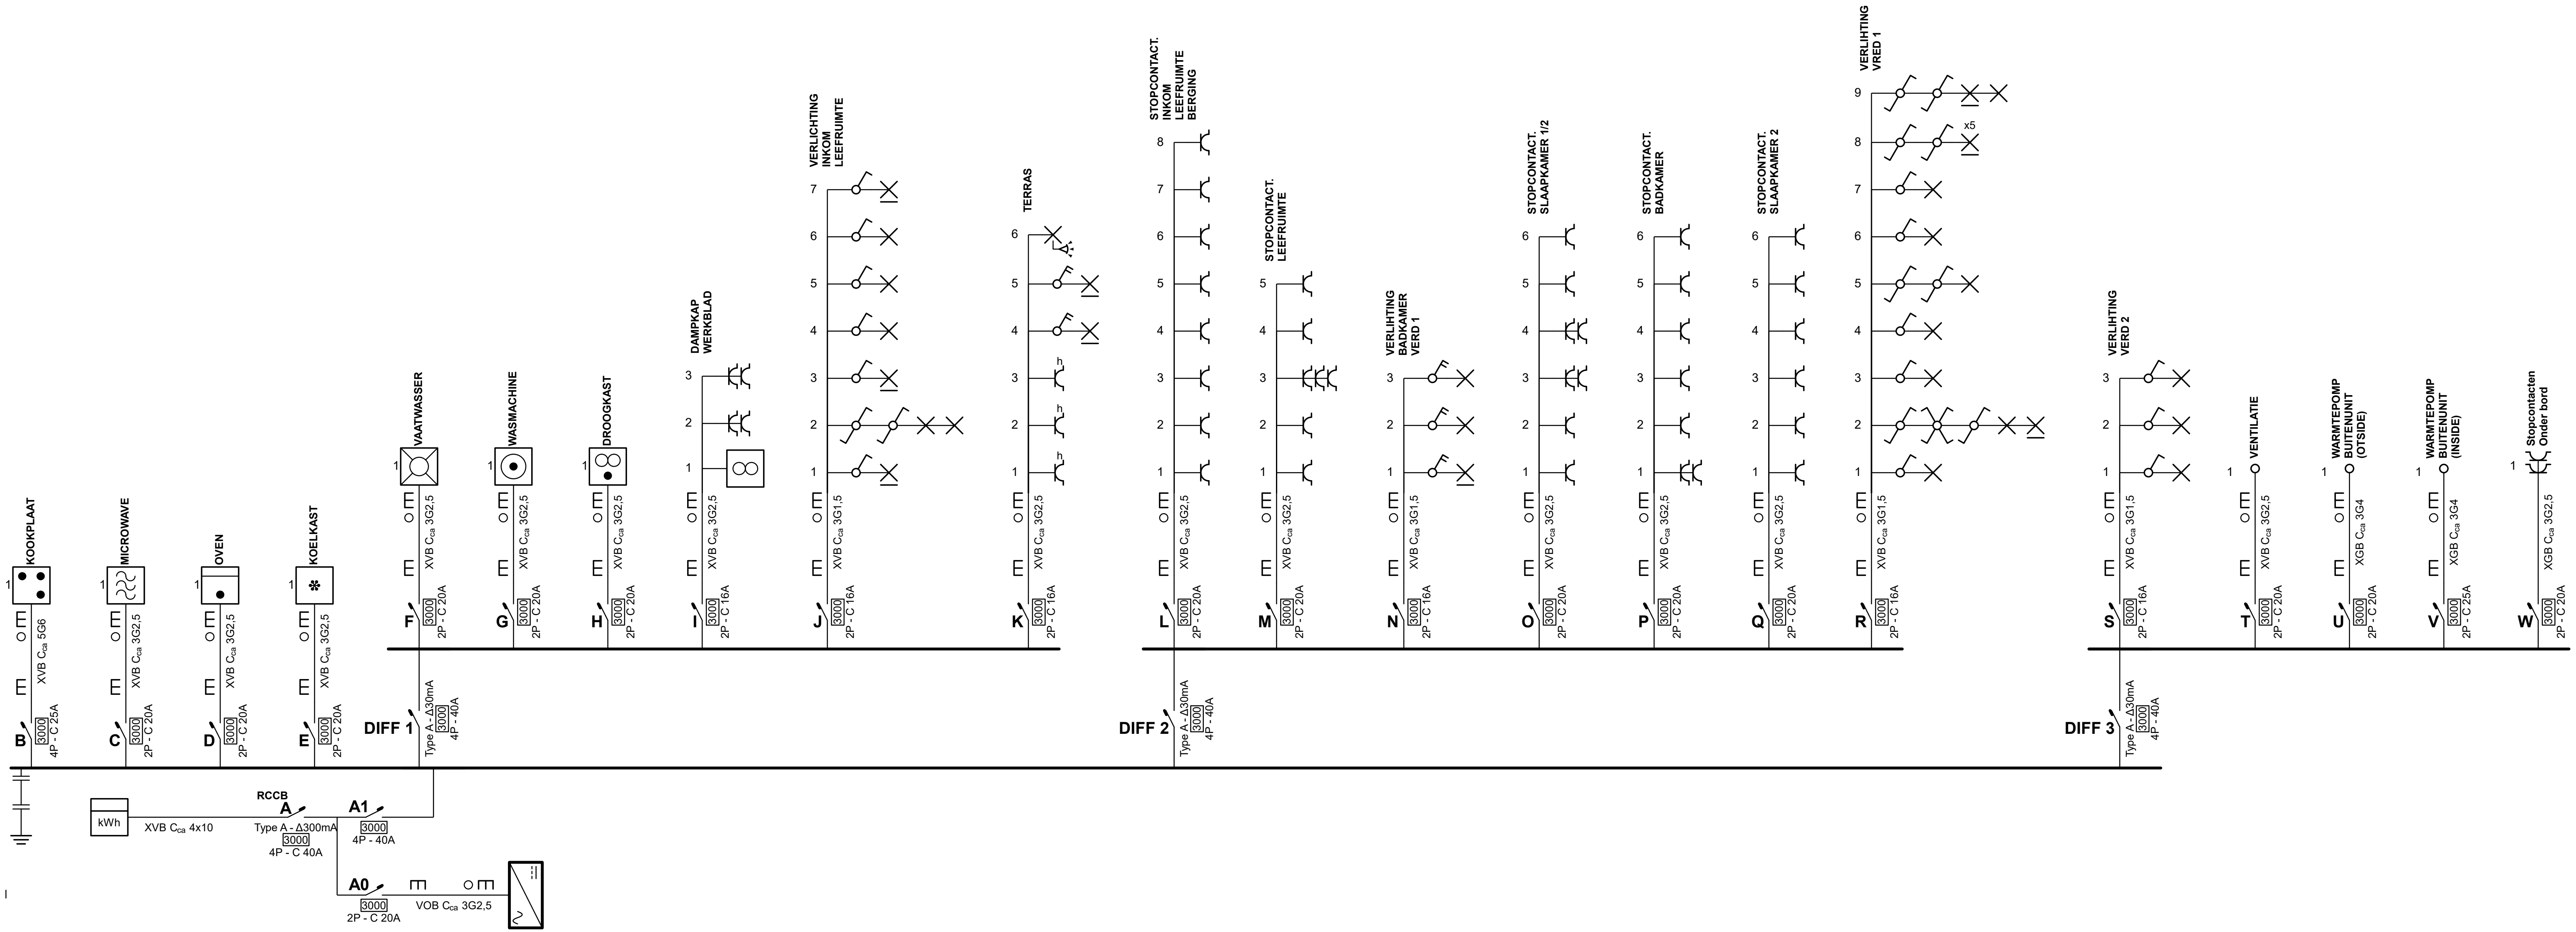
KOOKPLAAT
XVB C_{ca} 5G6
B
3000
4P - C 25A
MICROWAVE
XVB C_{ca} 3G2,5
C
3000
2P - C 20A
OVEN
XVB C_{ca} 3G2,5
D
3000
2P - C 20A
KOELKAST
XVB C_{ca} 3G2,5
E
3000
2P - C 20A
DIFF 1
Type A - Δ30mA
3000
4P - 40A
VAATWASSER
XVB C_{ca} 3G2,5
F
3000
2P - C 20A
WASMACHINE
XVB C_{ca} 3G2,5
G
3000
2P - C 20A
DROOGKAST
XVB C_{ca} 3G2,5
H
3000
2P - C 20A
DAMPKAP
WERKBLAD
XVB C_{ca} 3G2,5
I
3000
2P - C 16A
VERLICHTING
INKOM
LEEFRUIMTE
XVB C_{ca} 3G1,5
J
3000
2P - C 16A
TERRAS
XVB C_{ca} 3G2,5
K
3000
2P - C 16A
DIFF 2
Type A - Δ30mA
3000
4P - 40A
STOPCONTACT.
INKOM
LEEFRUIMTE
BERGING
XVB C_{ca} 3G2,5
L
3000
2P - C 20A
STOPCONTACT.
LEEFRUIMTE
XVB C_{ca} 3G2,5
M
3000
2P - C 20A
VERLIHTING
BADKAMER
VERD 1
XVB C_{ca} 3G1,5
N
3000
2P - C 16A
STOPCONTACT.
SLAAPKAMER 1/2
XVB C_{ca} 3G2,5
O
3000
2P - C 20A
STOPCONTACT.
BADKAMER
XVB C_{ca} 3G2,5
P
3000
2P - C 20A
STOPCONTACT.
SLAAPKAMER 2
XVB C_{ca} 3G2,5
Q
3000
2P - C 20A
VERLIHTING
VRED 1
x5
XVB C_{ca} 3G1,5
R
3000
2P - C 16A
DIFF 3
Type A - Δ30mA
3000
4P - 40A
VERLIHTING
VERD 2
XVB C_{ca} 3G1,5
S
3000
2P - C 16A
VENTILATIE
XVB C_{ca} 3G2,5
T
3000
2P - C 20A
WARMTEPOMP
BUITENUNIT
(OTSIDE)
XGB C_{ca} 3G4
U
3000
2P - C 20A
WARMTEPOMP
BUITENUNIT
(INSIDE)
XGB C_{ca} 3G4
V
3000
2P - C 25A
Stopcontacten
Onder bord
XGB C_{ca} 3G2,5
W
3000
2P - C 20A
kWh
XVB C_{ca} 4x10
RCCB
A
Type A - Δ300mA
3000
4P - C 40A
A1
3000
4P - 40A
A0
3000
2P - C 20A
VOB C_{ca} 3G2,5