A1 - Light wall

Bar area

LED 1 H-1200
LED 2 H-1700

Entrance

A1 Rail

A2 - Rail

A3 - Rail

Desk

A1 Rail

LED

Kitchen island

QX7
fridge drinks

QX6
fridge

A4 Rail

A4 Rail

A4

A4

Livingroom

A4 Rail

A4 Rail

Hallway

WC 1

WC 2

restroom

corridor

WC 3

Meeting room

Technical room

Lift

Lift board

Reception

stairway

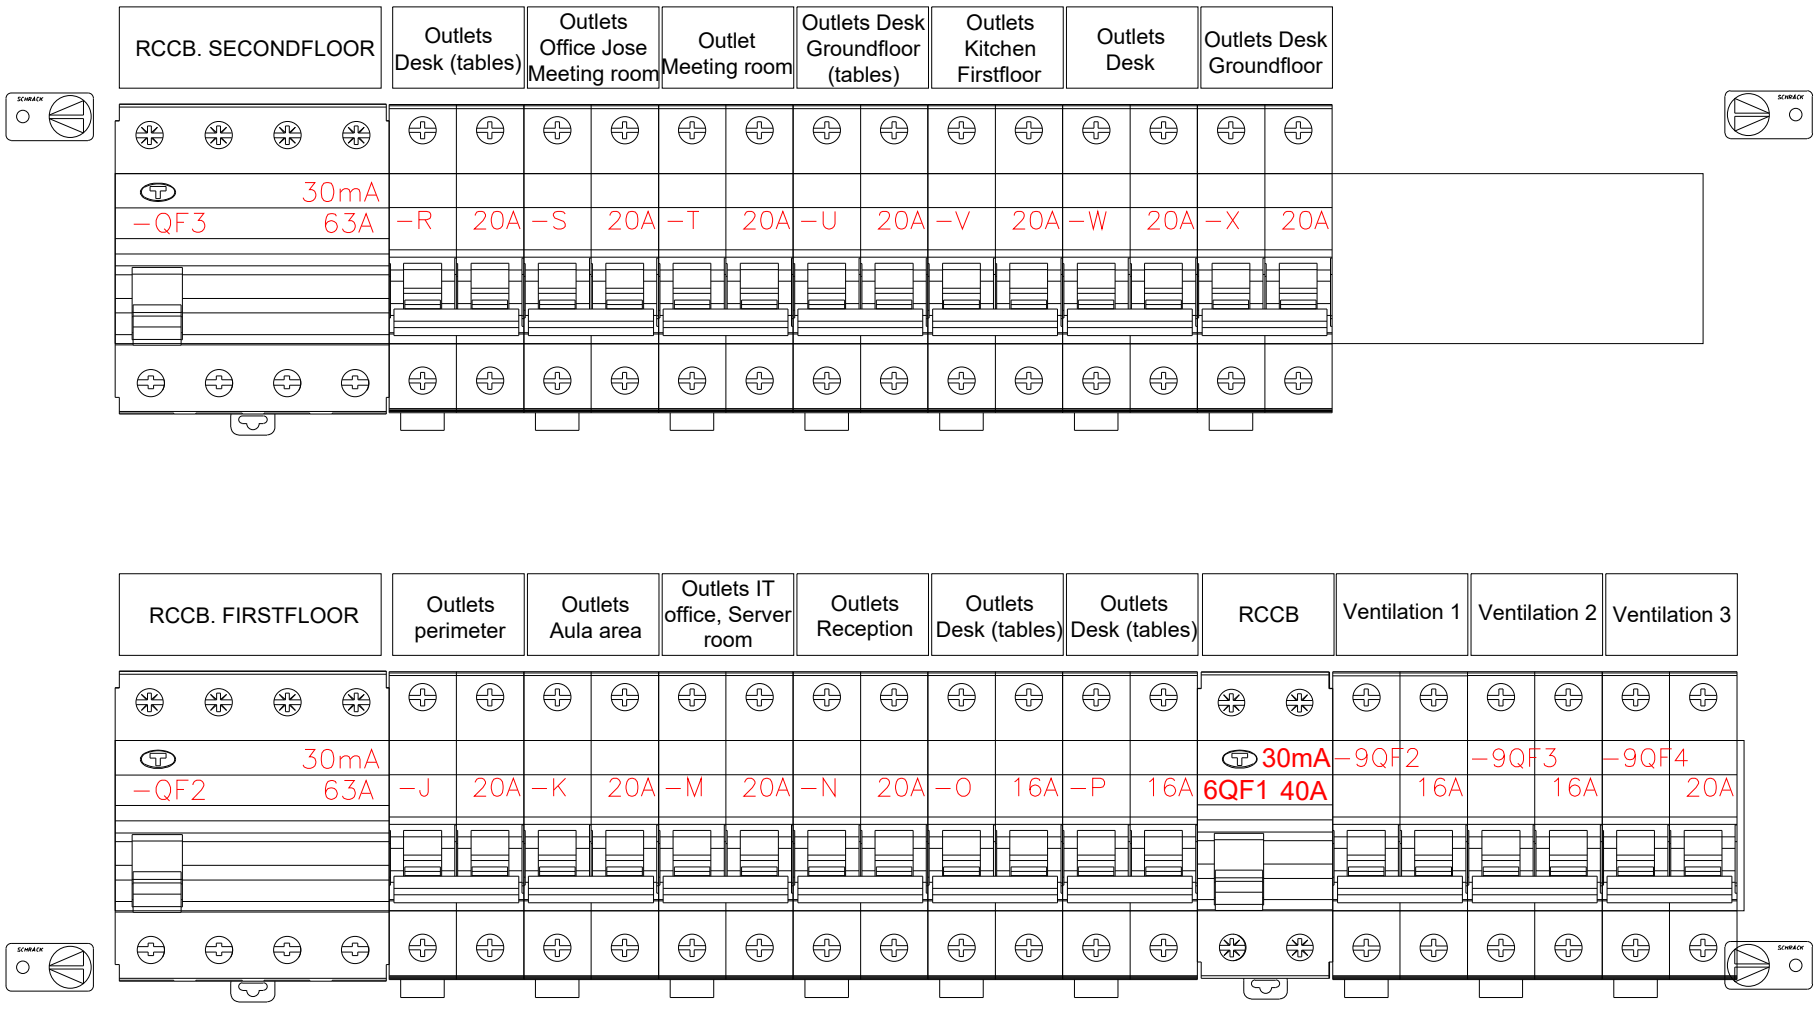
Rail - A4

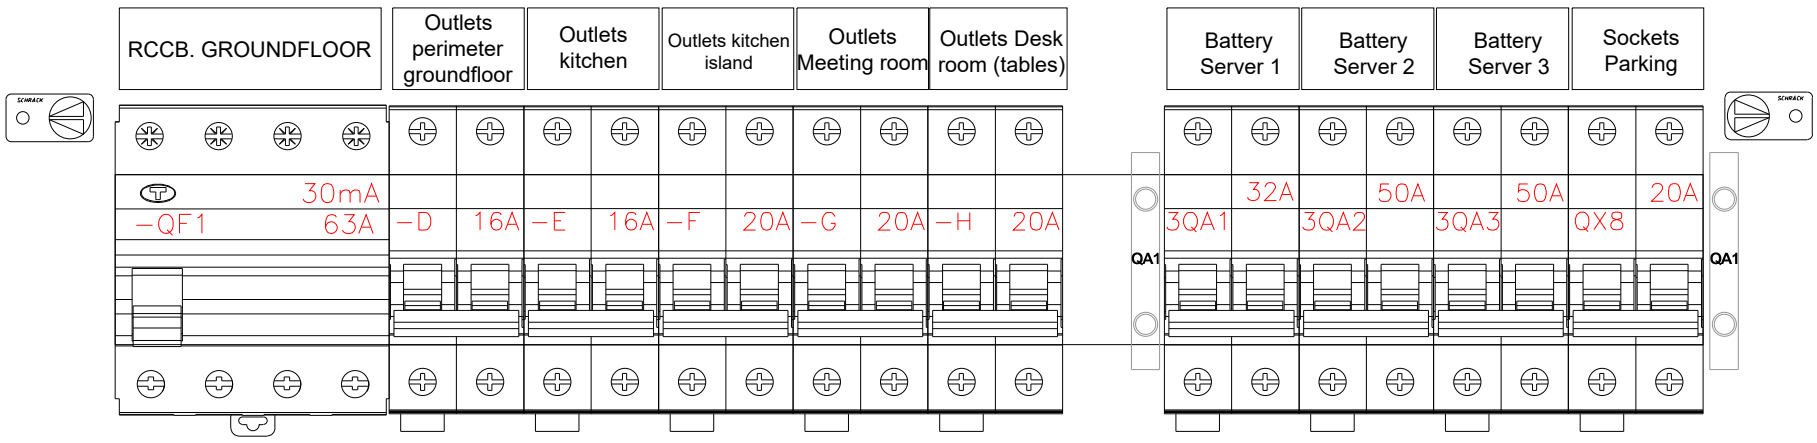
LED- QX10.1

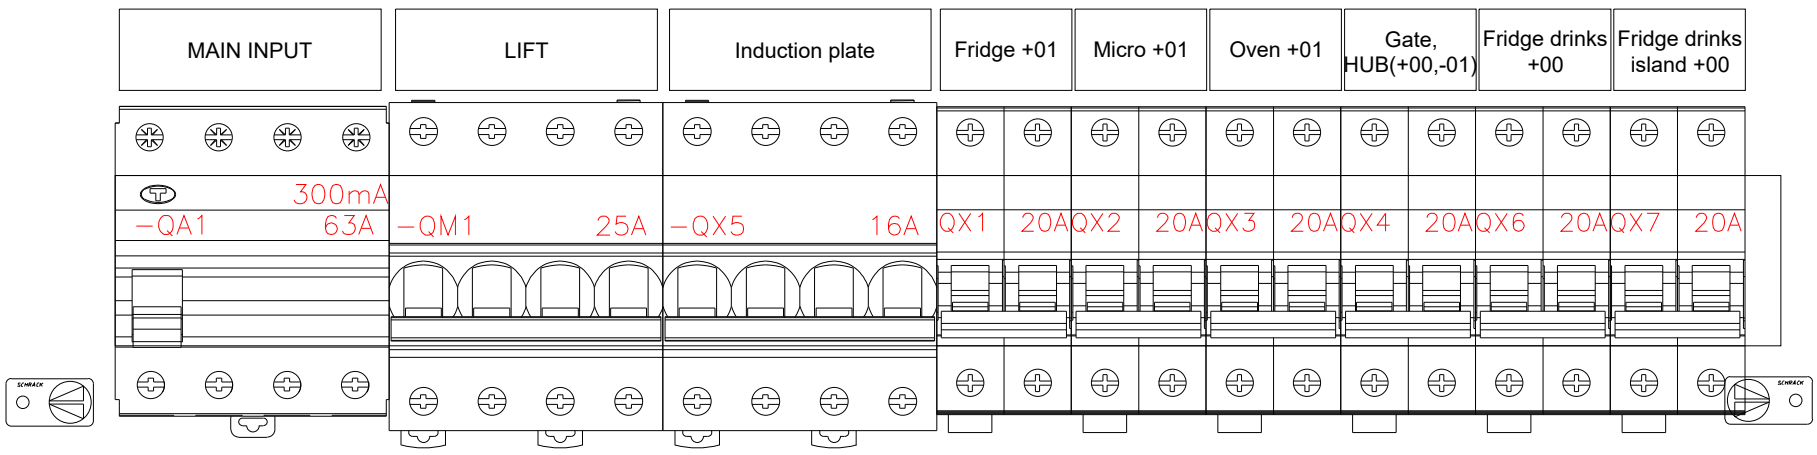
LED- QX10.1

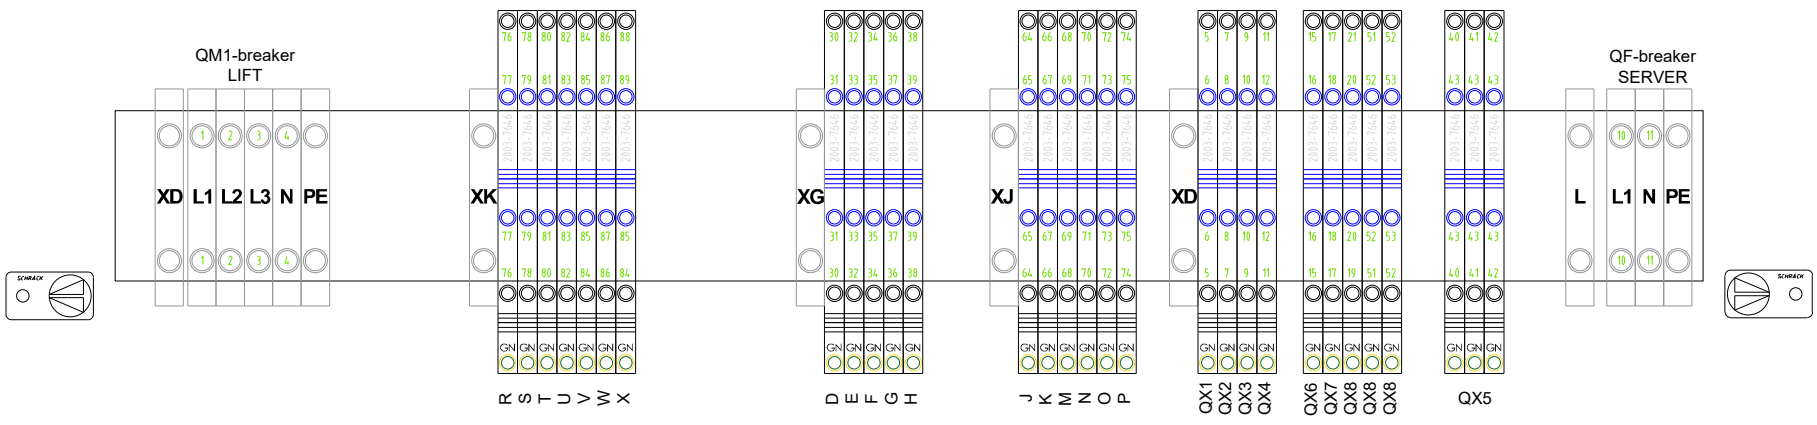
A1,A2,A3,A4
ALL OFF
Stairway

1.A EL


RCCB. SECONDFLOOR
Outlets Desk (tables)
Outlets Office Jose Meeting room
Outlet Meeting room
Outlets Desk Groundfloor (tables)
Outlets Kitchen Firstfloor
Outlets Desk
Outlets Desk Groundfloor
30mA
−QF3
63A
−R 20A
−S 20A
−T 20A
−U 20A
−V 20A
−W 20A
−X 20A
RCCB. FIRSTFLOOR
Outlets perimeter
Outlets Aula area
Outlets IT office, Server room
Outlets Reception
Outlets Desk (tables)
Outlets Desk (tables)
RCCB
Ventilation 1
Ventilation 2
Ventilation 3
30mA
−QF2
63A
−J 20A
−K 20A
−M 20A
−N 20A
−O 16A
−P 16A
30mA
6QF1 40A
−9QF2
16A
−9QF3
16A
−9QF4
20A


RCCB. GROUNDFLOOR
Outlets perimeter groundfloor
Outlets kitchen
Outlets kitchen island
Outlets Meeting room
Outlets Desk room (tables)
Battery Server 1
Battery Server 2
Battery Server 3
Sockets Parking
30mA
−QF1
63A
−D 16A
−E 16A
−F 20A
−G 20A
−H 20A
32A
3QA1
50A
3QA2
50A
3QA3
QX8
20A
QA1
QA1


MAIN INPUT
LIFT
Induction plate
Fridge +01
Micro +01
Oven +01
Gate, HUB(+00,-01)
Fridge drinks +00
Fridge drinks island +00
300mA
−QA1
63A
−QM1 25A
−QX5 16A
QX1 20A
QX2 20A
QX3 20A
QX4 20A
QX6 20A
QX7 20A


QM1-breaker
LIFT
XD L1 L2 L3 N PE
XK
XG
XJ
XD
QF-breaker
SERVER
L L1 N PE
R S T U V W X
D E F G H
J K M N O P
QX1 QX2 QX3 QX4
QX6 QX7 QX8 QX8
QX5